


ISOMETRIC (NOT TO SCALE)

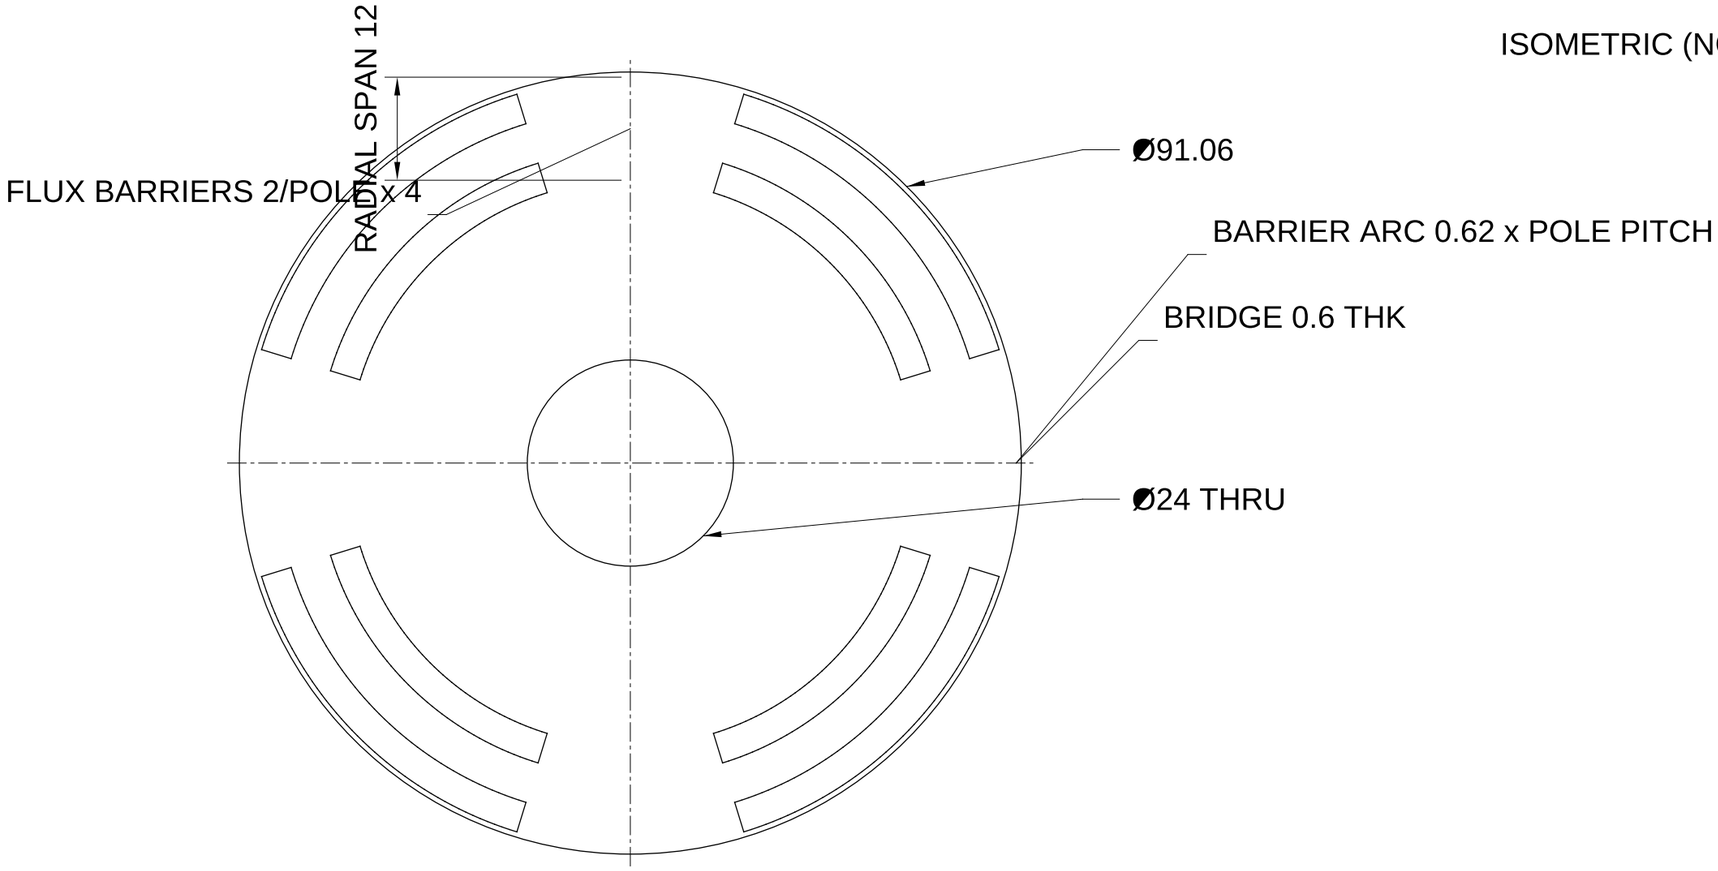

PLAN (CROSS-SECTION)

NOTES: 1. LAMINATION THICKNESS NOMINAL 0.5 mm - PENDING PURCHASE SPEC
2. GEOMETRY: COMMITTED D-010 BASELINE. ALL NON-DIMENSIONED VALUES FROM MODEL.
3. BARRIERS CENTRED ON Q-AXIS (LAMINATION TOPOLOGY). FEM ROTOR POSITIONS ARE SOLVE STATES, NOT LAMINATION FEATURES.

ROTOR LAMINATION - M1 SYNRM v1 (D-010)	SCALE 1.4:1 MM THIRD ANGLE
M-43 ELECTRICAL STEEL (INDICATIVE - D-009) · Project M1	SHEET 1 OF 1 REV 0 rotor_lamination_drawing