
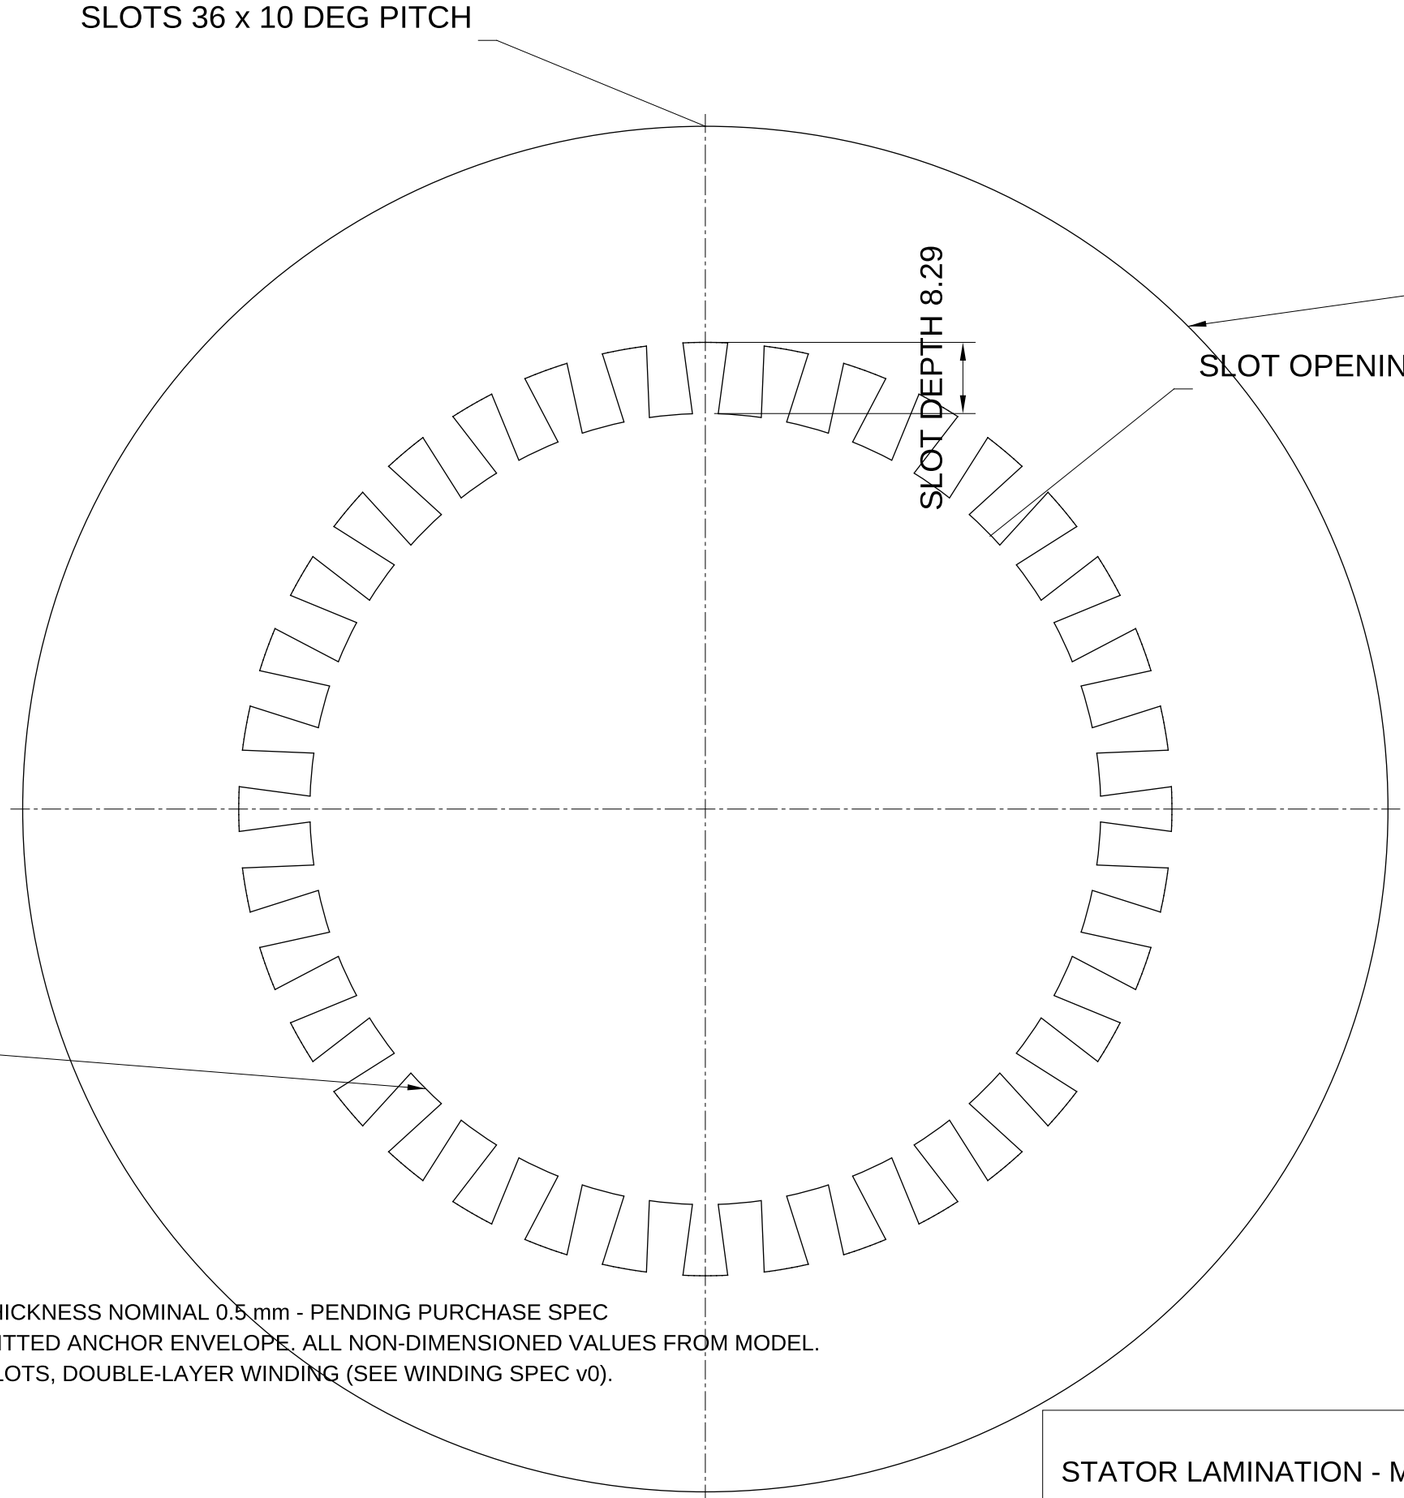


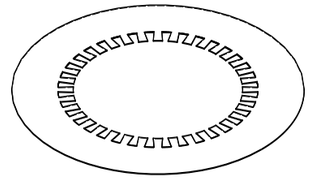

ISOMETRIC (NOT TO SCALE)

PLAN (CROSS-SECTION)

NOTES: 1. LAMINATION THICKNESS NOMINAL 0.5 mm - PENDING PURCHASE SPEC
2. GEOMETRY: COMMITTED ANCHOR ENVELOPE. ALL NON-DIMENSIONED VALUES FROM MODEL.
3. 36 SEMI-CLOSED SLOTS, DOUBLE-LAYER WINDING (SEE WINDING SPEC v0).

STATOR LAMINATION - M1 SYNRM v1 (D-010)	SCALE 1.4:1 MM THIRD ANGLE
M-43 ELECTRICAL STEEL (INDICATIVE - D-009) · Project M1	SHEET 1 OF 1 REV 0 stator_lamination_drawing